Projeto dos armários — marcenaria

Planta com os armários numerados · medidas em cm · conferir no local antes de produzir



Quadro de armários

Nº	Armário · parede	L × A × P	h instal.	Frentes
1	Bancada em L (canto) Parede direita (janelão) · 310.5 a 452.5 cm da frente (vidro)	142 × 90 × 64	piso	2P 3G
2	Bancada em L (canto) Parede direita (janelão) · 528.5 a 577.5 cm da frente (vidro)	49 × 90 × 64	piso	1P
3	Bancada da pia (granilite) Parede do fundo (pia) · 173 a 288 cm da parede da suíte	115 × 90 × 62	piso	2P
4	Bancada em L (canto) Parede do fundo (pia) · 288 a 428 cm da parede da suíte	140 × 90 × 62	piso	3G
5	Armário baixo ao lado do buffet Parede da suíte (esquerda) · 12.5 a 132.5 cm da frente (vidro)	120 × 86 × 56	piso	3G
6	Torre lava-louças (alta) Parede do fundo (pia) · 108 a 173 cm da parede da suíte	65 × 269 × 62	piso	2P 1G
7	Armário sobre geladeira/freezer Parede da suíte (esquerda) · 336 a 540 cm da frente (vidro)	204 × 60 × 44	205	4P
8	Armário em L – lateral Parede direita (janelão) · 530 a 605 cm da frente (vidro)	75 × 109 × 35	160	2P
9	Armário em L – fundo (até a janela) Parede do fundo (pia) · 305.5 a 428 cm da parede da suíte	122,5 × 109 × 35	160	2P 1N
10	Nichos de temperos – lateral (até a parede do fundo) Parede direita (janelão) · 530 a 640 cm da frente (vidro)	110 × 36 × 20	124	3N

Especificações gerais


- Caixas e frentes em MDF 18 mm (ou madeira maciça) com acabamento amadeirado rústico — madeira serrada clara com nós aparentes (ver foto de referência).
- Puxadores tipo flor/roseta em ferro preto envelhecido (1 por frente; posição indicada nas vistas).
- Dobradiças com amortecimento; corrediças telescópicas para gavetas; gavetas finas para talheres/temperos.
- Rodapé recuado (5 cm) em MDF escuro. Fundo dos nichos em madeira escura.
- Tampos das bancadas em granilite avermelhado 3 cm — fornecidos pelo marmorista (ver folha de tampos).
- P = porta · G = gaveta · N = nicho aberto. Vistas frontais desenhadas como vistas de quem está de frente para o armário.



Referência de acabamento

1 — Bancada em L (canto)

Parede direita (janelão) · 310.5 a 452.5 cm da frente (vidro) · apoiado no piso

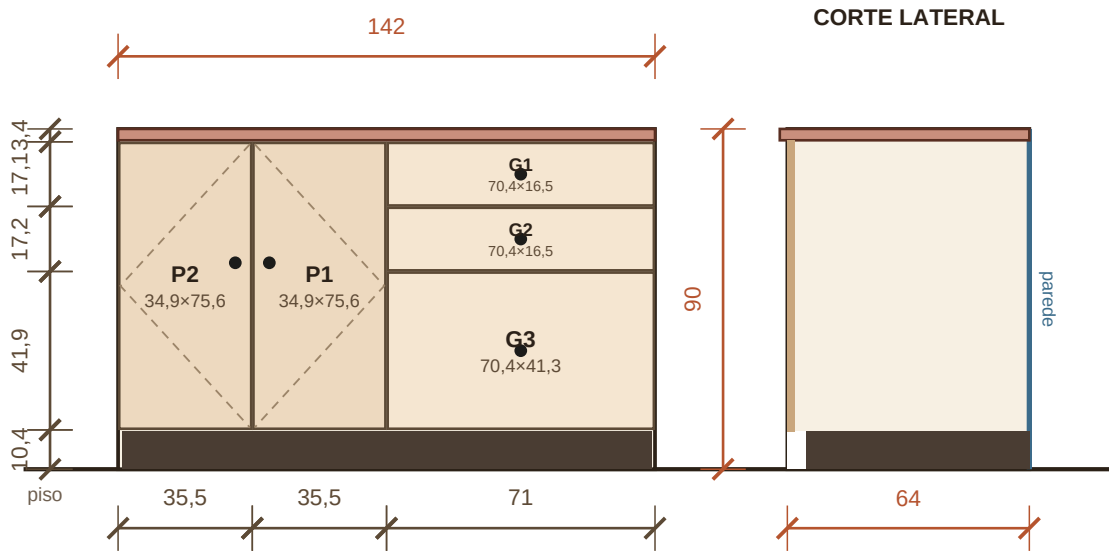

Especificação


Medida externa	142 (L) × 90 (A) × 64 (P) cm
Instalação	piso
Rodapé	10 cm, recuado 5 cm
Tampo	3 cm (granilite — marmorista)
Frentes	2 porta(s) · 3 gaveta(s) · 0 nicho(s)
Puxadores	5 un. (flor, ferro preto)

Frentes (L × A, cm)

G1	gaveta · 70,4 × 16,5
G2	gaveta · 70,4 × 16,5
G3	gaveta · 70,4 × 41,3
P1	porta · 34,9 × 75,6
P2	porta · 34,9 × 75,6

2 — Bancada em L (canto)

Parede direita (janelão) · 528.5 a 577.5 cm da frente (vidro) · apoiado no piso

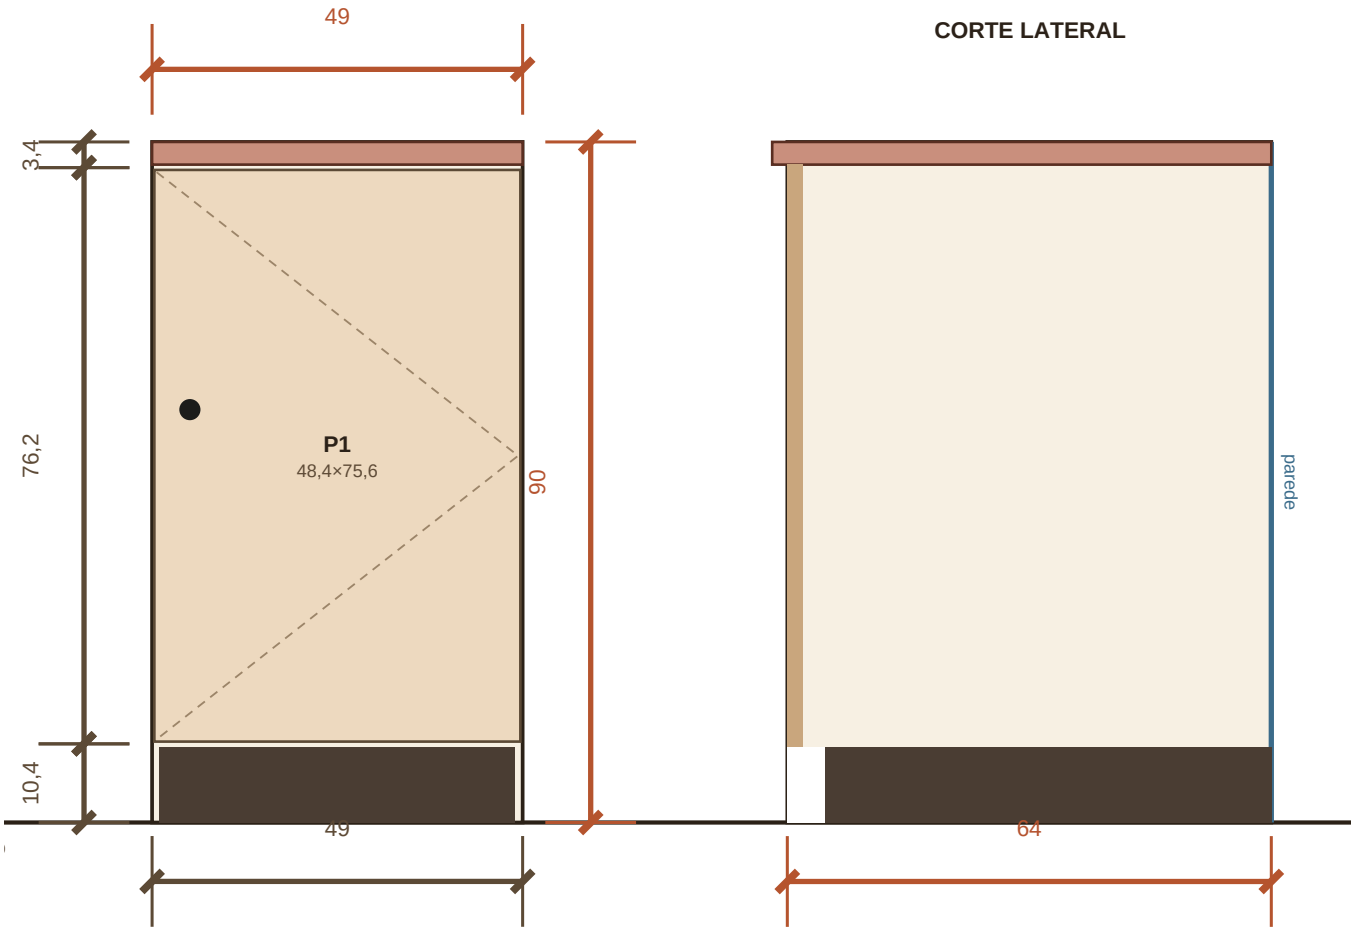

Especificação

Medida externa	49 (L) × 90 (A) × 64 (P) cm
Instalação	piso
Rodapé	10 cm, recuado 5 cm
Tampo	3 cm (granilite — marmorista)
Frentes	1 porta(s) · 0 gaveta(s) · 0 nicho(s)
Puxadores	1 un. (flor, ferro preto)


Frentes (L × A, cm)

P1 porta · 48,4 × 75,6

Vista frontal e corte lateral · escala 1:10 (A4)

3 — Bancada da pia (granilite)

Parede do fundo (pia) · 173 a 288 cm da parede da suíte · apoiado no piso

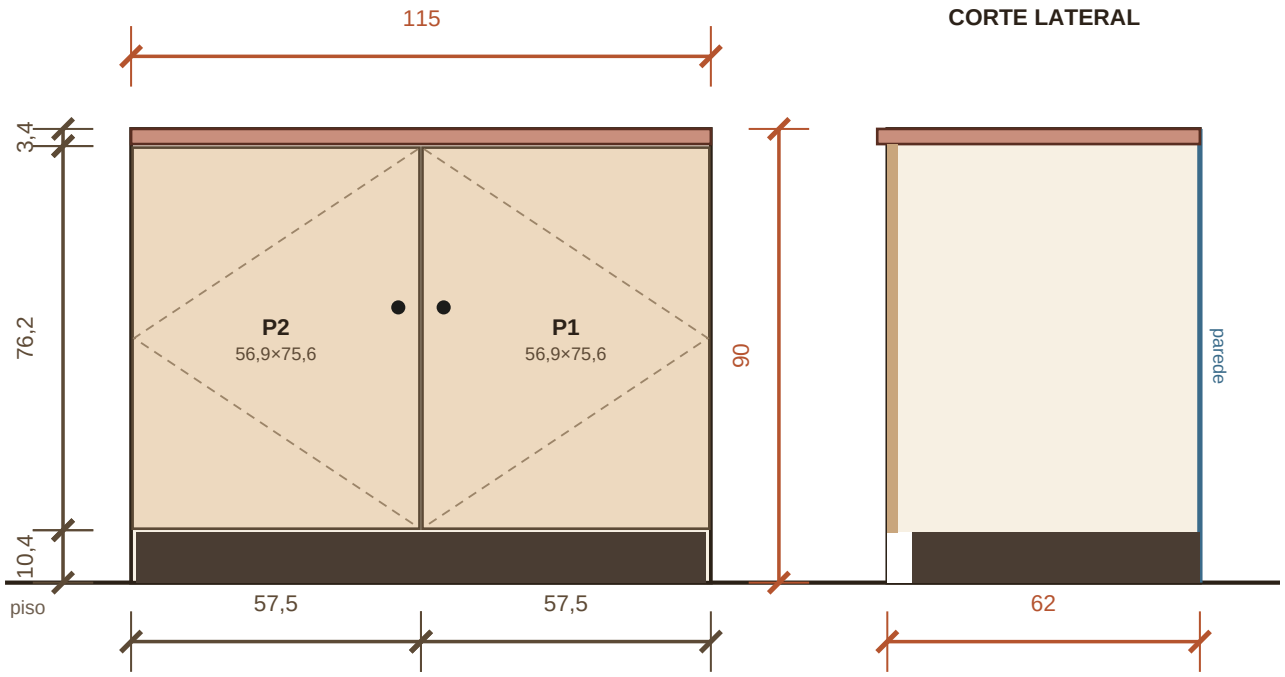

Especificação

Medida externa	115 (L) × 90 (A) × 62 (P) cm
Instalação	piso
Rodapé	10 cm, recuado 5 cm
Tampo	3 cm (granilite — marmorista)
Frentes	2 porta(s) · 0 gaveta(s) · 0 nicho(s)
Puxadores	2 un. (flor, ferro preto)

Frentes (L × A, cm)


P1	porta · 56,9 × 75,6
P2	porta · 56,9 × 75,6

Observações

• Gabinete sob cuba 70×40 cm: corpo sem tampo, portas (sem gavetas); prever passagem de hidráulica.

4 — Bancada em L (canto)

Parede do fundo (pia) · 288 a 428 cm da parede da suíte · apoiado no piso

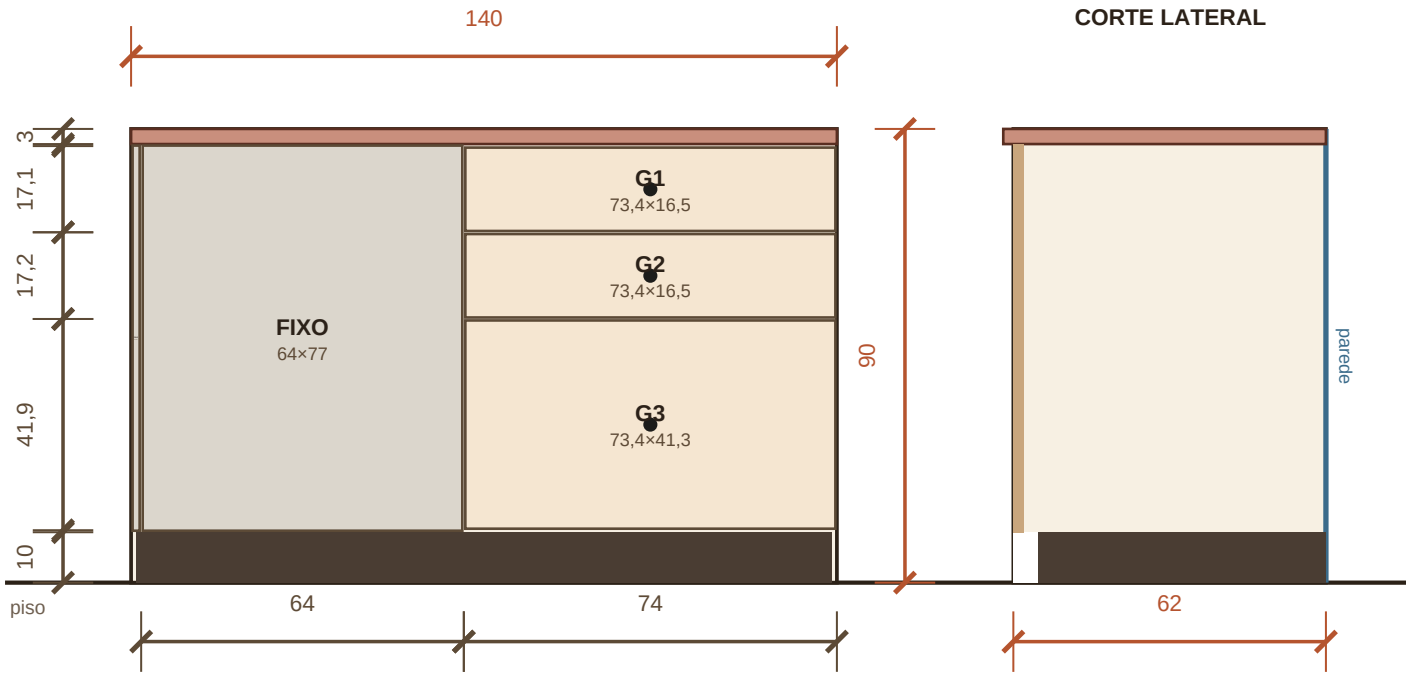

Especificação

Medida externa	140 (L) × 90 (A) × 62 (P) cm
Instalação	piso
Rodapé	10 cm, recuado 5 cm
Tampo	3 cm (granilite — marmorista)
Frentes	0 porta(s) · 3 gaveta(s) · 0 nicho(s)
Puxadores	3 un. (flor, ferro preto)

Frentes (L × A, cm)


G1	gaveta · 73,4 × 16,5
G2	gaveta · 73,4 × 16,5
G3	gaveta · 73,4 × 41,3

Observações

• Canto cego: trecho da frente encoberto pelo móvel vizinho fica fechado (painel fixo).

5 — Armário baixo ao lado do buffet

Parede da suíte (esquerda) · 12.5 a 132.5 cm da frente (vidro) · apoiado no piso

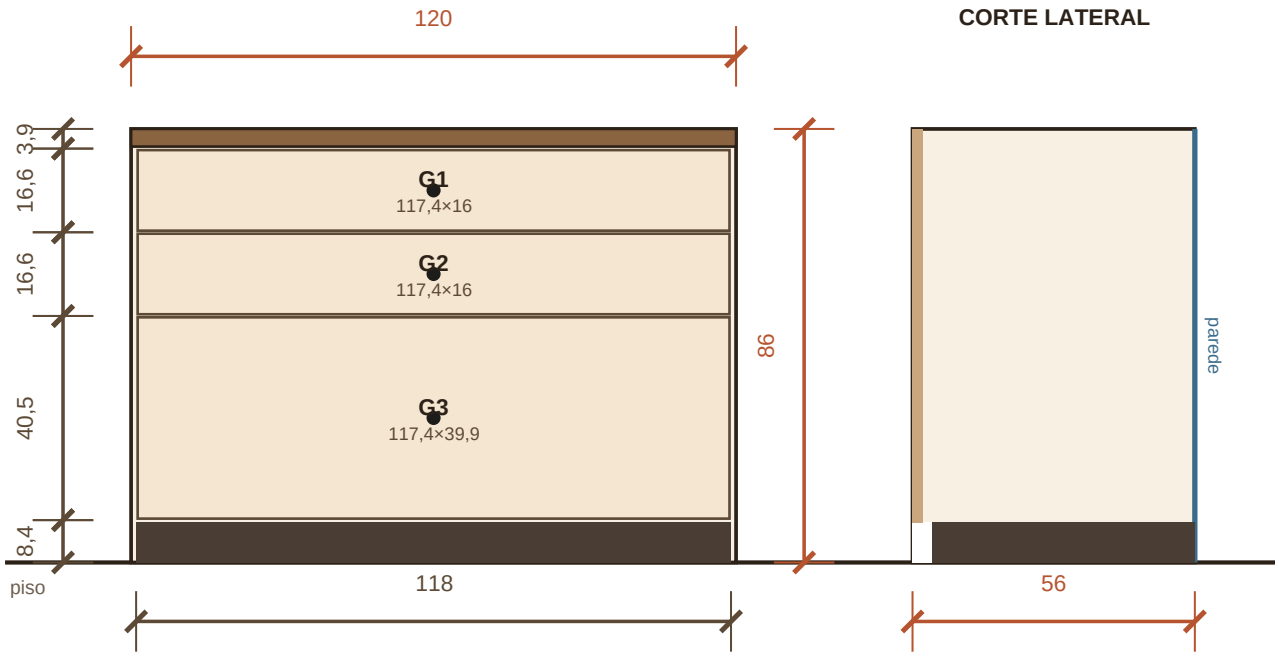

Especificação

Medida externa	120 (L) × 86 (A) × 56 (P) cm
Instalação	piso
Rodapé	8 cm, recuado 4 cm
Tampo	3.5 cm (madeira, mesmo acabamento)
Frentes	0 porta(s) · 3 gaveta(s) · 0 nicho(s)
Puxadores	3 un. (flor, ferro preto)


Frentes (L × A, cm)

G1	gaveta · 117,4 × 16
G2	gaveta · 117,4 × 16
G3	gaveta · 117,4 × 39,9

Vista frontal e corte lateral · escala 1:15 (A4)

6 — Torre lava-louças (alta)

Parede do fundo (pia) · 108 a 173 cm da parede da suíte · apoiado no piso

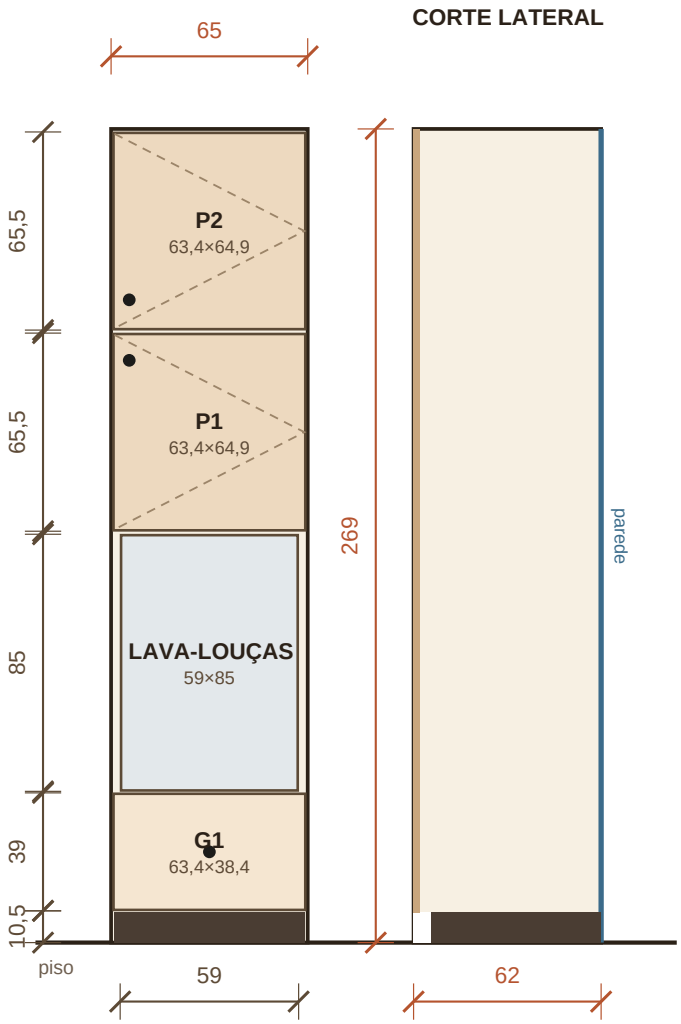

Especificação

Medida externa	65 (L) × 269 (A) × 62 (P) cm
Instalação	piso
Rodapé	10 cm, recuado 6 cm
Frentes	2 porta(s) · 1 gaveta(s) · 0 nicho(s)
Puxadores	3 un. (flor, ferro preto)

Frentes (L × A, cm)

G1	gaveta · 63,4 × 38,4
P1	porta · 63,4 × 64,9
P2	porta · 63,4 × 64,9


Observações

• Vão para lava-louças embutida: 60 × 86 cm (aparelho 59 × 85 × 59), base a 50 cm do piso; prever ponto de água, esgoto e tomada.

Vista frontal e corte lateral · escala 1:25 (A4)

7 — Armário sobre geladeira/freezer

Parede da suíte (esquerda) · 336 a 540 cm da frente (vidro) · instalado a 205 cm do piso

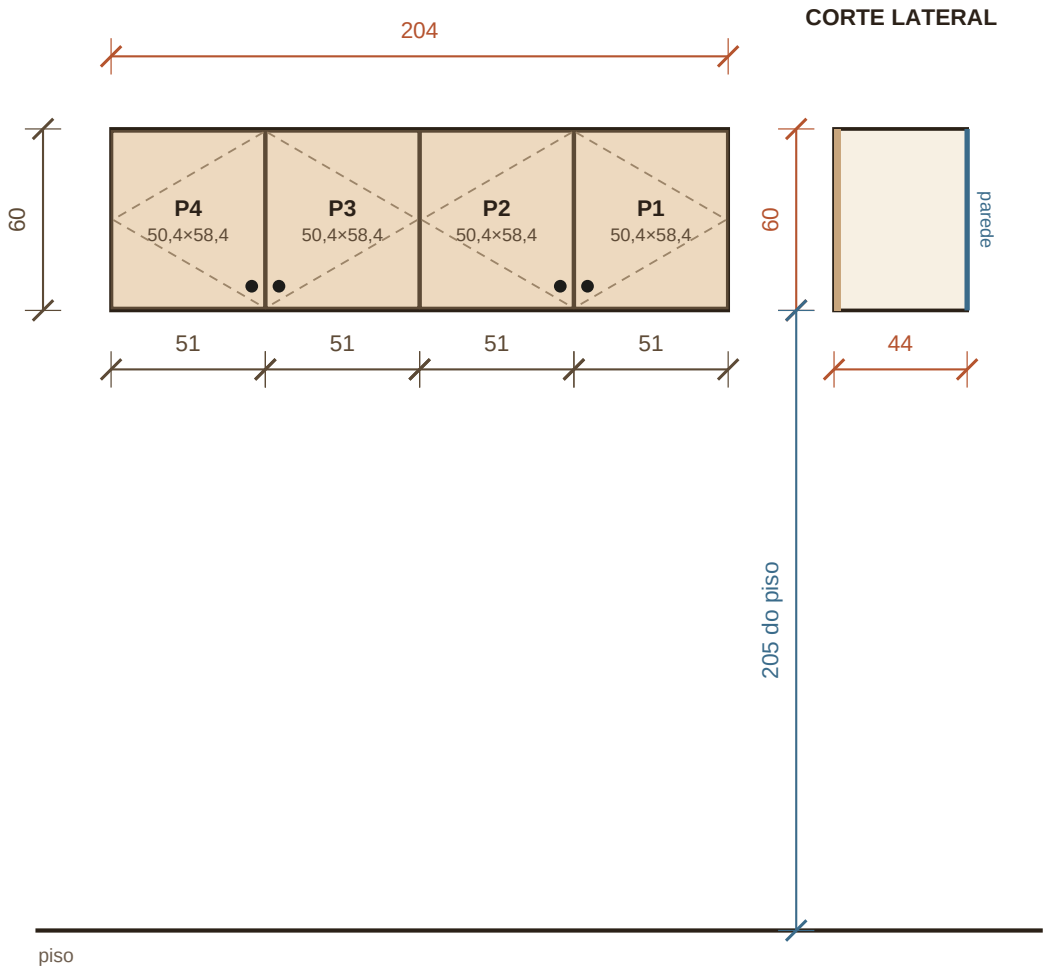

Especificação


Medida externa	204 (L) × 60 (A) × 44 (P) cm
Instalação	suspenso, base a 205 cm do piso
Fixação	trilho/suporte oculto na parede
Frentes	4 porta(s) · 0 gaveta(s) · 0 nicho(s)
Puxadores	4 un. (flor, ferro preto)

Frentes (L × A, cm)

P1	porta · 50,4 × 58,4
P2	porta · 50,4 × 58,4
P3	porta · 50,4 × 58,4
P4	porta · 50,4 × 58,4

8 — Armário em L – lateral

Parede direita (janelão) · 530 a 605 cm da frente (vidro) · instalado a 160 cm do piso

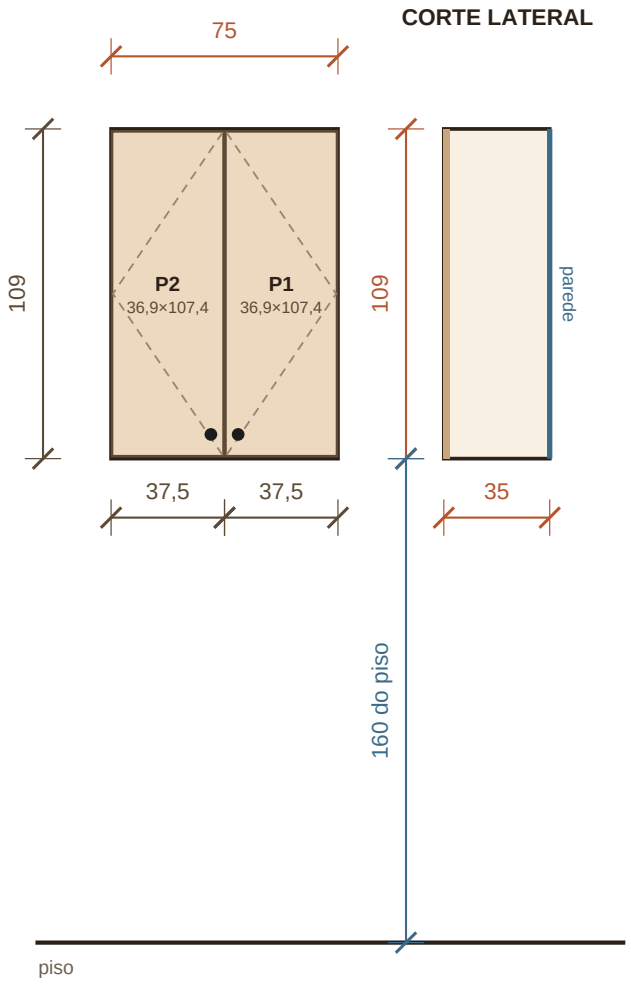

Especificação


Medida externa	75 (L) × 109 (A) × 35 (P) cm
Instalação	suspenso, base a 160 cm do piso
Fixação	trilho/suporte oculto na parede
Frentes	2 porta(s) · 0 gaveta(s) · 0 nicho(s)
Puxadores	2 un. (flor, ferro preto)

Frentes (L × A, cm)

P1	porta · 36,9 × 107,4
P2	porta · 36,9 × 107,4

9 — Armário em L – fundo (até a janela)

Parede do fundo (pia) · 305.5 a 428 cm da parede da suíte · instalado a 160 cm do piso

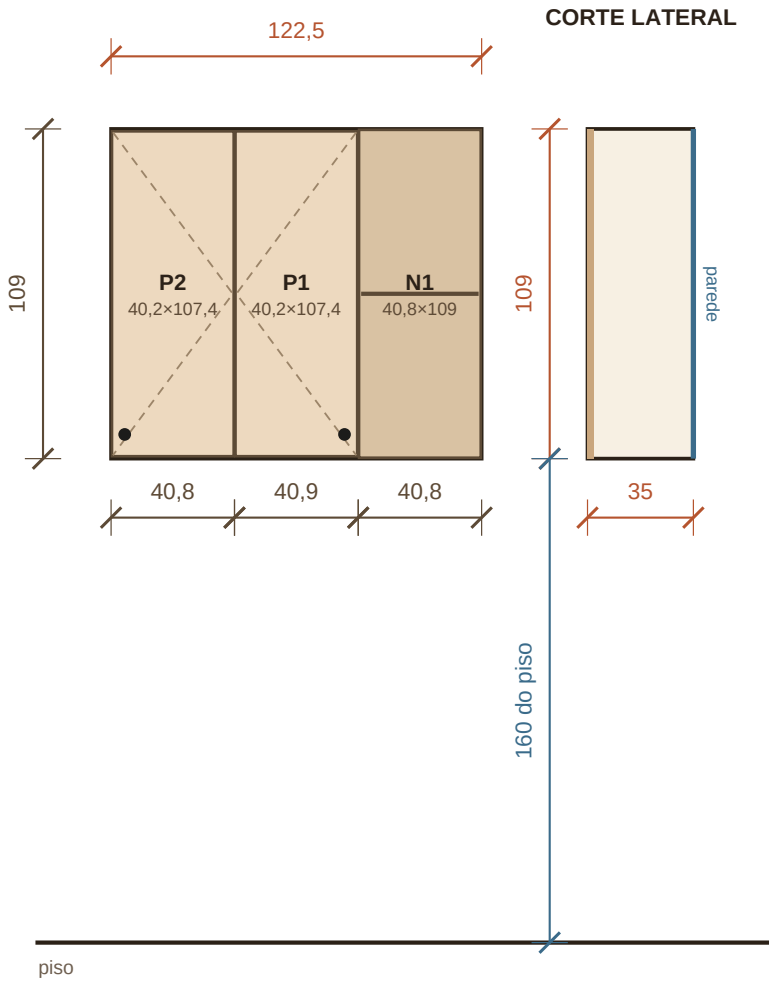

Especificação

Medida externa	122,5 (L) × 109 (A) × 35 (P) cm
Instalação	suspenso, base a 160 cm do piso
Fixação	trilho/suporte oculto na parede
Frentes	2 porta(s) · 0 gaveta(s) · 1 nicho(s)
Puxadores	2 un. (flor, ferro preto)

Frentes (L × A, cm)


N1	vão aberto · 40,2 × 108,4 · 1 prateleira
P1	porta · 40,2 × 107,4
P2	porta · 40,2 × 107,4

Observações

- Vão(s) de nicho aberto com 1 prateleira no meio, fundo em madeira escura.

10 — Nichos de temperos – lateral (até a parede do fundo)

Parede direita (janelão) · 530 a 640 cm da frente (vidro) · instalado a 124 cm do piso

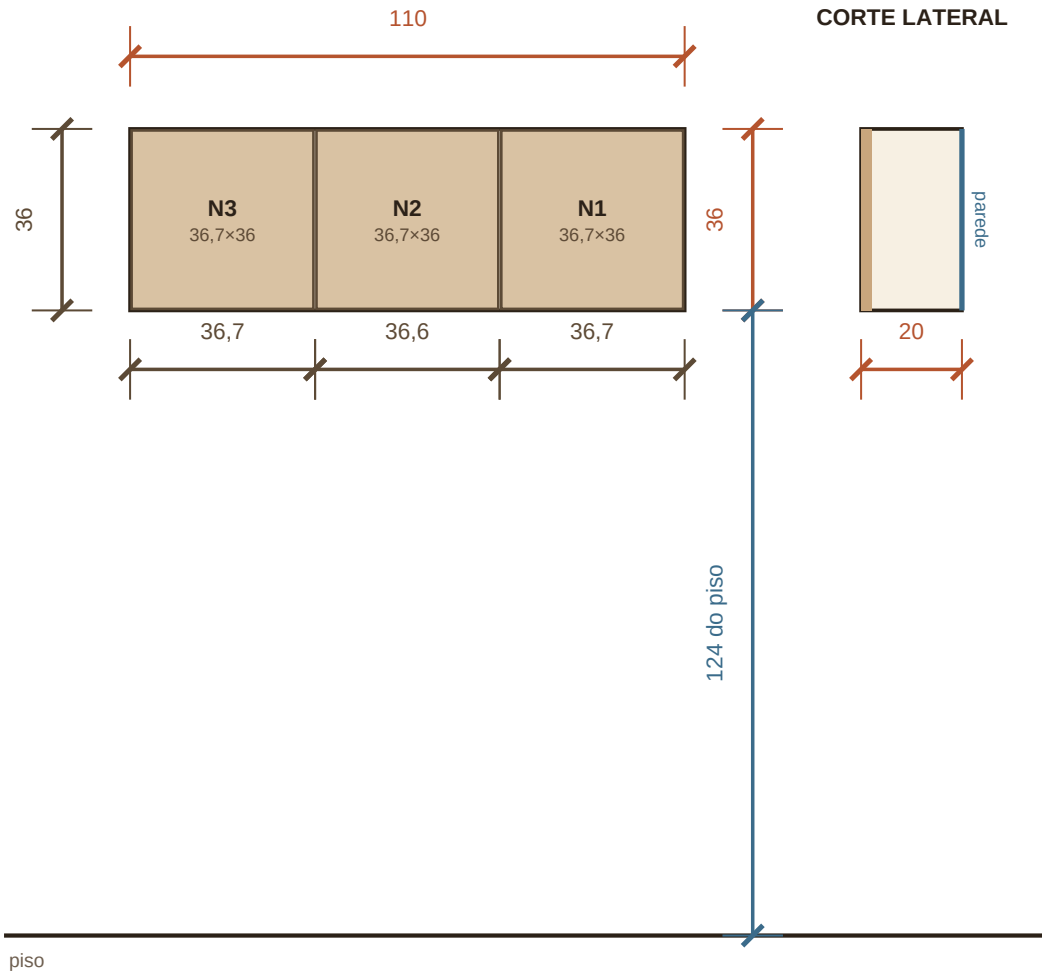

Especificação

Medida externa	110 (L) × 36 (A) × 20 (P) cm
Instalação	suspenso, base a 124 cm do piso
Fixação	parafusado na parede (sem portas)
Frentes	0 porta(s) · 0 gaveta(s) · 3 nicho(s)
Puxadores	0 un. (flor, ferro preto)

Frentes (L × A, cm)

N1	vão aberto · 36,1 × 35,4
N2	vão aberto · 36,1 × 35,4
N3	vão aberto · 36,1 × 35,4

Observações

• Nicho aberto para temperos: 3 vão(s), sem prateleira intermediária, chapas de 2 cm, fundo de 1,2 cm.

Lista de frentes (portas, gavetas) e caixas

Projeto de marcenaria · Cozinha & Copa · 08/11/2026

Medidas das frentes já descontadas as folgas de 3 mm de cada lado · conferir no local

Tipo	Largura	Altura	Qtd.	Armários (Nº)
gaveta	73,5	41,5	1	4
gaveta	70,5	41,5	1	1
gaveta	117,5	40	1	5
gaveta	63,5	38,5	1	6
gaveta	73,5	16,5	2	4
gaveta	70,5	16,5	2	1
gaveta	117,5	16	2	5
porta	40	107,5	2	9
porta	37	107,5	2	8
porta	57	75,5	2	3
porta	48,5	75,5	1	2
porta	35	75,5	2	1
porta	63,5	65	2	6
porta	50,5	58,5	4	7

Total: 15 portas · 10 gavetas · 25 puxadores · 4 vãos de nicho

Caixas (medida externa)

Nº	Armário	L × A × P
1	Bancada em L (canto)	142 × 90 × 64
2	Bancada em L (canto)	49 × 90 × 64
3	Bancada da pia (granilite)	115 × 90 × 62
4	Bancada em L (canto)	140 × 90 × 62
5	Armário baixo ao lado do buffet	120 × 86 × 56
6	Torre lava-louças (alta)	65 × 269 × 62
7	Armário sobre geladeira/freezer	204 × 60 × 44
8	Armário em L – lateral	75 × 109 × 35
9	Armário em L – fundo (até a janela)	122,5 × 109 × 35
10	Nichos de temperos – lateral (até a parede do fundo)	110 × 36 × 20

Tampos em granilite avermelhado (marmorista)

Projeto de marcenaria · Cozinha & Copa · 08/11/2026

Espessura 3 cm · beiral frontal 2 cm · rodabanca 10 cm nas laterais encostadas na parede · medidas em cm

Nº	Bancada	Tampo L × P × esp.	Recortes / rebaixo	Rodabanca
1	Bancada em L (canto)	142 × 66 × 3	—	sem rodabanca
2	Bancada em L (canto)	49 × 66 × 3	—	fundo 49 cm
3	Bancada da pia (granilite)	115 × 64 × 3	cuba: recorte 66 × 36 a 14 da borda esq. (vista de cima); rebaixo 1,5 cm em volta (esq 4, dir 78, frente 3.5, fundo 7.5)	fundo 115 cm
4	Bancada em L (canto)	140 × 64 × 3	—	fundo 140 cm + lateral 62 cm

Vista 3D de referência — cozinha

Imagem ilustrativa; prevalecem as medidas das folhas técnicas



Vista 3D de referência — lateral

Imagem ilustrativa; prevalecem as medidas das folhas técnicas

