Cabinet plans — carpentry

Plan with numbered cabinets · dimensions in cm · check on site before producing



Cabinet schedule

No.	Cabinet · wall	W × H × D	install h.	Fronts
1	L-shaped counter (corner) Right wall (large window) · 310.5 to 452.5 cm from the front (glass)	142 × 90 × 64	floor	2P 3G
2	L-shaped counter (corner) Right wall (large window) · 528.5 to 577.5 cm from the front (glass)	49 × 90 × 64	floor	1P
3	Sink counter (granilite) Back wall (sink) · 173 to 288 cm from the suite wall	115 × 90 × 62	floor	2P
4	L-shaped counter (corner) Back wall (sink) · 288 to 428 cm from the suite wall	140 × 90 × 62	floor	3G
5	Low cabinet next to the sideboard Suite wall (left) · 12.5 to 132.5 cm from the front (glass)	120 × 86 × 56	floor	3G
6	Dishwasher tower (tall) Back wall (sink) · 108 to 173 cm from the suite wall	65 × 269 × 62	floor	2P 1G
7	Cabinet above fridge/freezer Suite wall (left) · 336 to 540 cm from the front (glass)	204 × 60 × 44	205	4P
8	L-shaped cabinet – side Right wall (large window) · 530 to 605 cm from the front (glass)	75 × 109 × 35	160	2P
9	L-shaped cabinet – back (up to the window) Back wall (sink) · 305.5 to 428 cm from the suite wall	122.5 × 109 × 35	160	2P 1N
10	Spice niches – side (up to the back wall) Right wall (large window) · 530 to 640 cm from the front (glass)	110 × 36 × 20	124	3N

General specifications


- Carcasses and fronts in 18 mm MDF (or solid wood) with a rustic wood finish — light sawn timber with visible knots (see reference photo).
- Flower/rosette pulls in aged black iron (1 per front; position shown in the views).
- Soft-close hinges; telescopic slides for drawers; shallow drawers for cutlery/spices.
- Recessed plinth (5 cm) in dark MDF. Niche backs in dark wood.
- Countertops in reddish granilite, 3 cm — supplied by the stonemason (see countertop sheet).
- D = door · Dw = drawer · N = open niche. Front views are drawn as seen by someone standing in front of the cabinet.



Finish reference

1 — L-shaped counter (corner)

Right wall (large window) · 310.5 to 452.5 cm from the front (glass) · standing on the floor

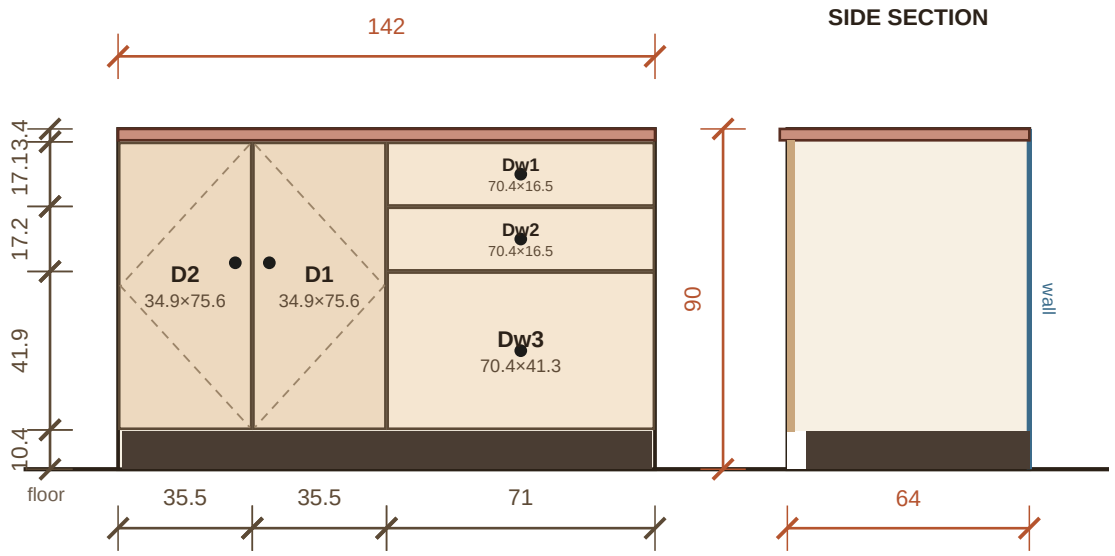

Specification


Overall size	142 (W) × 90 (H) × 64 (D) cm
Installation	floor
Plinth	10 cm, recessed 5 cm
Countertop	3 cm (granilite — by the stonemason)
Fronts	2 door(s) · 3 drawer(s) · 0 niche(s)
Pulls	5 pcs (flower, black iron)

Fronts (W × H, cm)

Dw1	drawer · 70.4 × 16.5
Dw2	drawer · 70.4 × 16.5
Dw3	drawer · 70.4 × 41.3
D1	door · 34.9 × 75.6
D2	door · 34.9 × 75.6

2 — L-shaped counter (corner)

Right wall (large window) · 528.5 to 577.5 cm from the front (glass) · standing on the floor

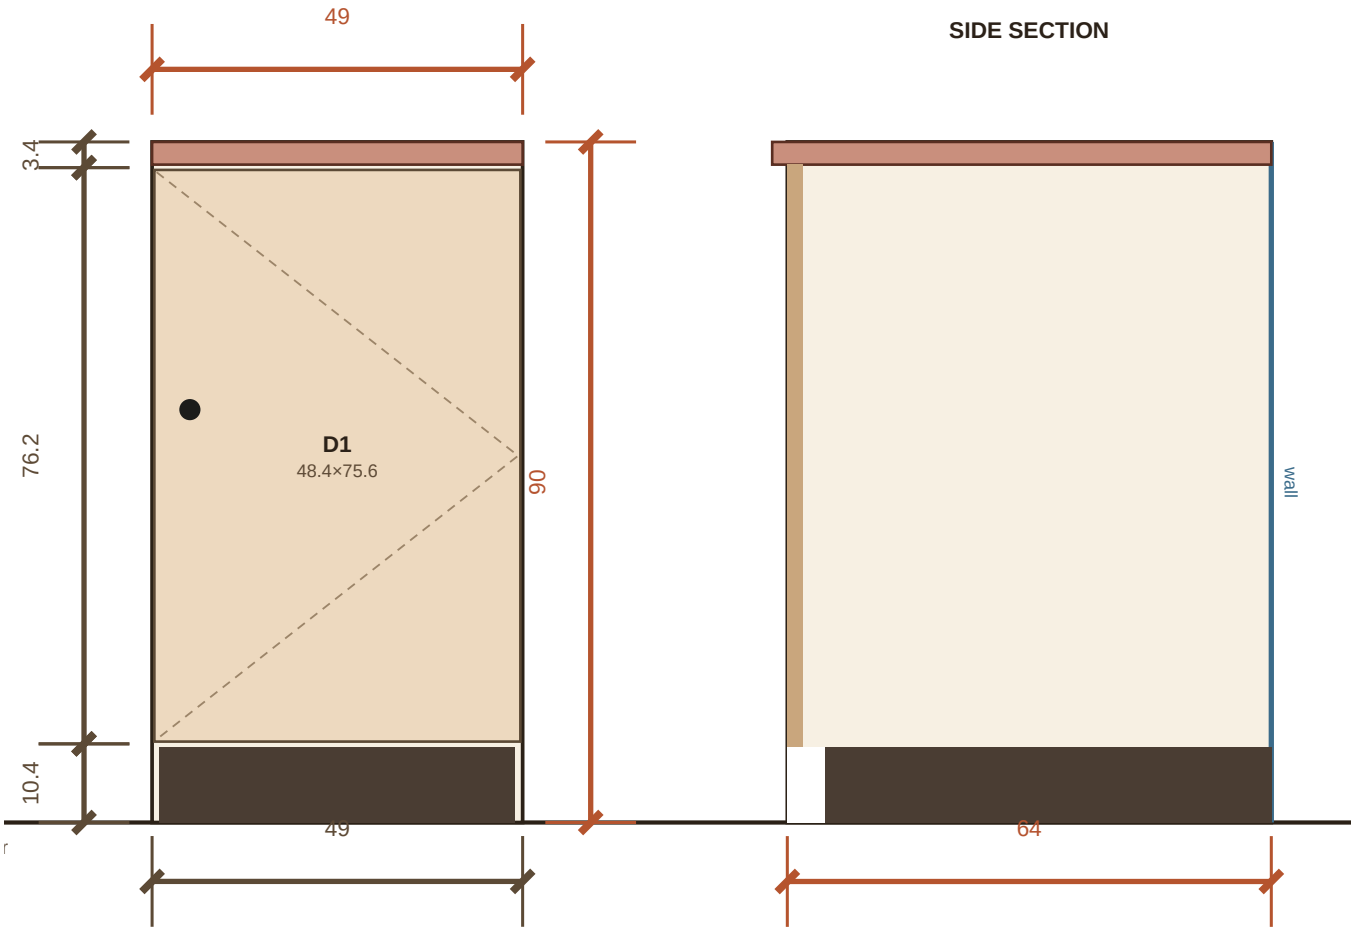

Specification

Overall size	49 (W) × 90 (H) × 64 (D) cm
Installation	floor
Plinth	10 cm, recessed 5 cm
Countertop	3 cm (granilite — by the stonemason)
Fronts	1 door(s) · 0 drawer(s) · 0 niche(s)
Pulls	1 pcs (flower, black iron)


Fronts (W × H, cm)

D1 door · 48.4 × 75.6

Front view and side section · scale 1:10 (A4)

3 — Sink counter (granilite)

Back wall (sink) · 173 to 288 cm from the suite wall · standing on the floor

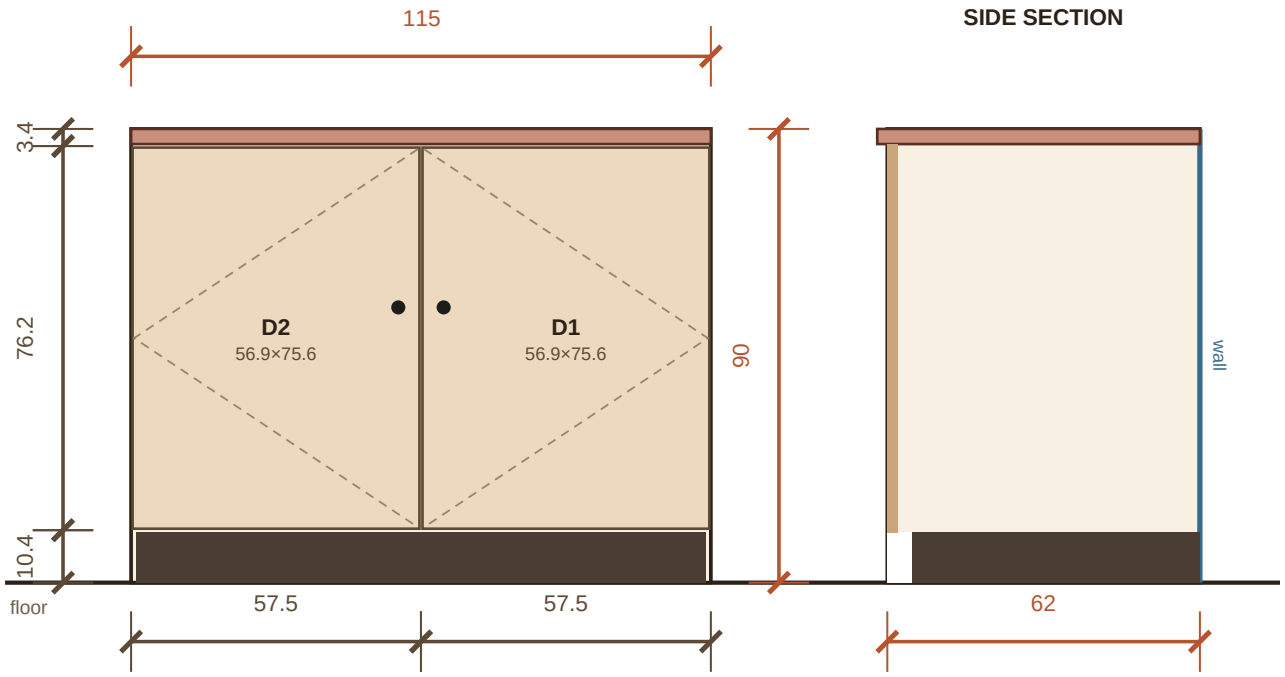

Specification

Overall size	115 (W) × 90 (H) × 62 (D) cm
Installation	floor
Plinth	10 cm, recessed 5 cm
Countertop	3 cm (granilite — by the stonemason)
Fronts	2 door(s) · 0 drawer(s) · 0 niche(s)
Pulls	2 pcs (flower, black iron)

Fronts (W × H, cm)


D1	door · 56.9 × 75.6
D2	door · 56.9 × 75.6

Notes

• Sink base 70×40 cm: carcass without a top, doors (no drawers); allow room for plumbing.

4 — L-shaped counter (corner)

Back wall (sink) · 288 to 428 cm from the suite wall · standing on the floor

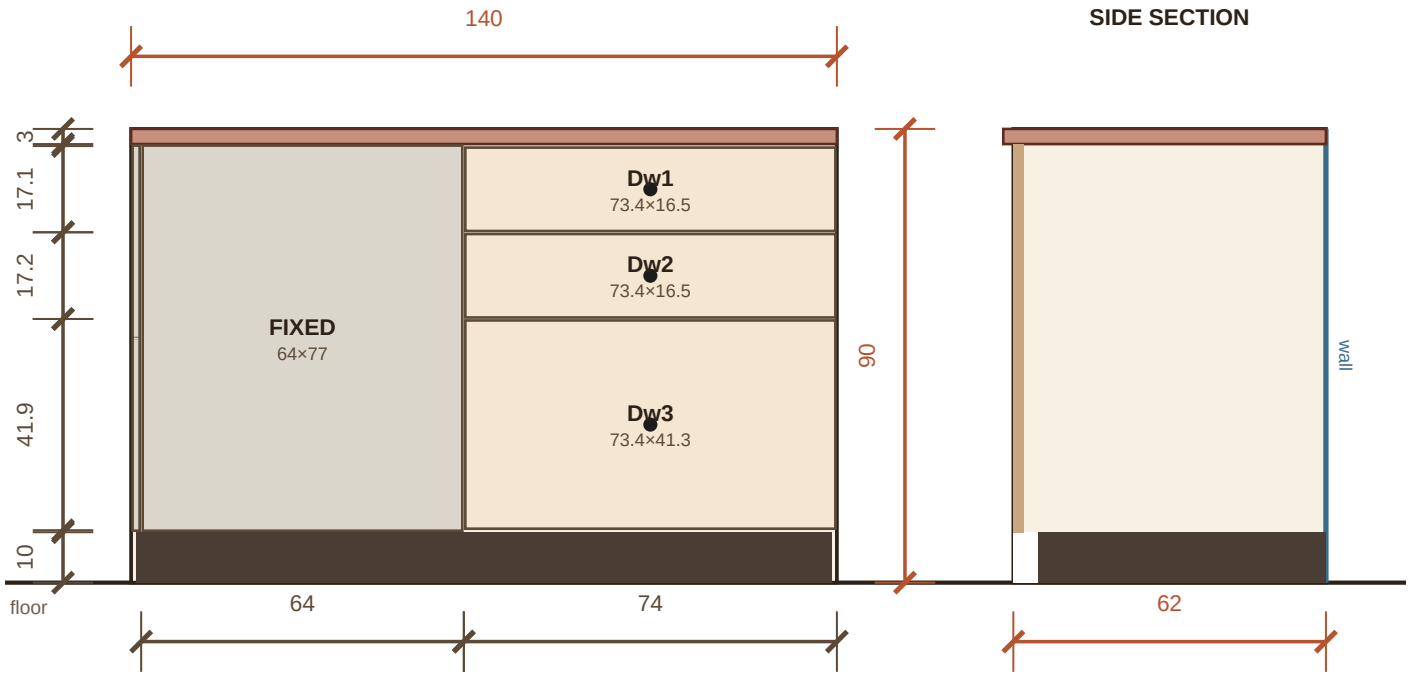

Specification

Overall size	140 (W) × 90 (H) × 62 (D) cm
Installation	floor
Plinth	10 cm, recessed 5 cm
Countertop	3 cm (granilite — by the stonemason)
Fronts	0 door(s) · 3 drawer(s) · 0 niche(s)
Pulls	3 pcs (flower, black iron)

Fronts (W × H, cm)


Dw1	drawer · 73.4 × 16.5
Dw2	drawer · 73.4 × 16.5
Dw3	drawer · 73.4 × 41.3

Notes

• Blind corner: the part of the front hidden by the neighbouring unit stays closed (fixed panel).

5 — Low cabinet next to the sideboard

Suite wall (left) · 12.5 to 132.5 cm from the front (glass) · standing on the floor

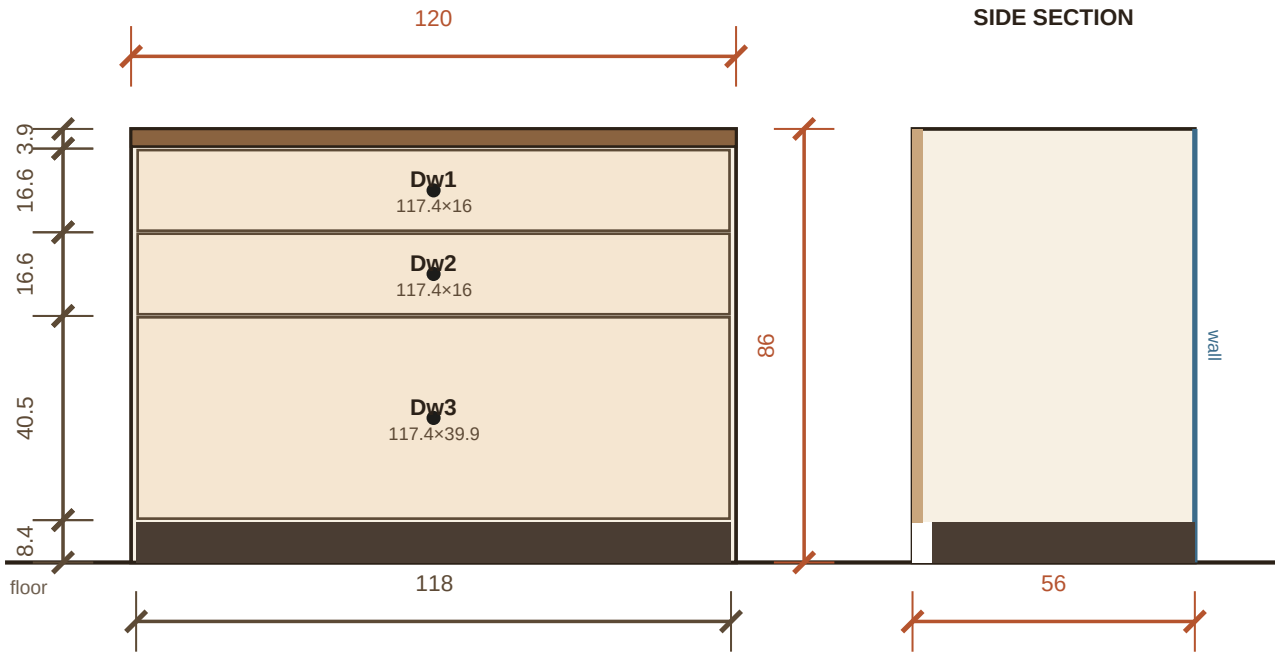

Specification


Overall size	120 (W) × 86 (H) × 56 (D) cm
Installation	floor
Plinth	8 cm, recessed 4 cm
Countertop	3.5 cm (wood, same finish)
Fronts	0 door(s) · 3 drawer(s) · 0 niche(s)
Pulls	3 pcs (flower, black iron)

Fronts (W × H, cm)

Dw1	drawer · 117.4 × 16
Dw2	drawer · 117.4 × 16
Dw3	drawer · 117.4 × 39.9

6 — Dishwasher tower (tall)

Back wall (sink) · 108 to 173 cm from the suite wall · standing on the floor

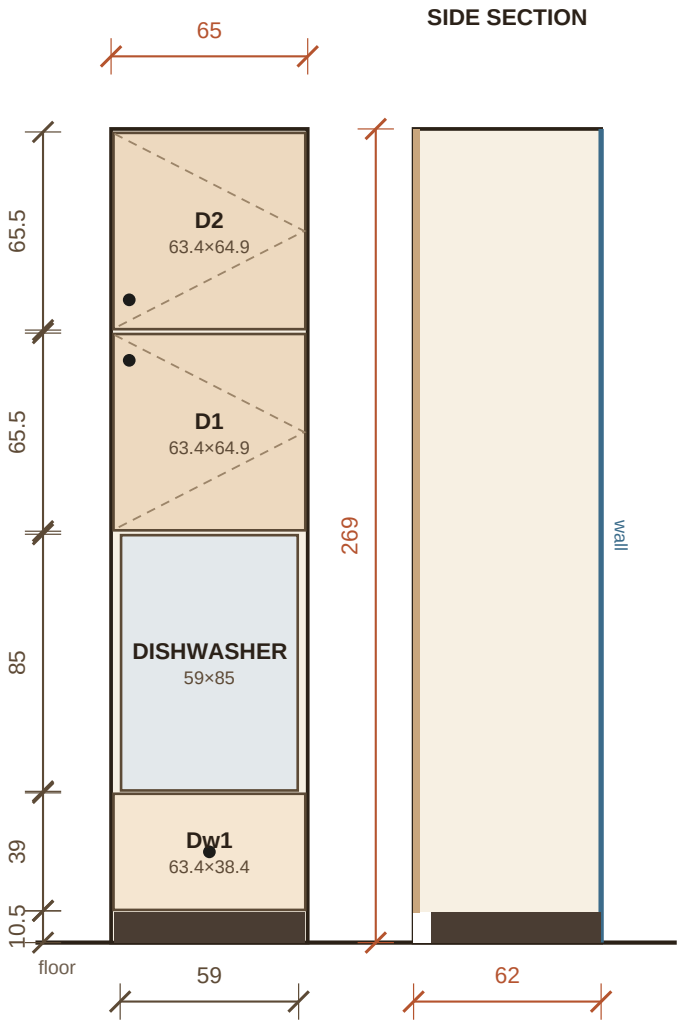

Specification

Overall size	65 (W) × 269 (H) × 62 (D) cm
Installation	floor
Plinth	10 cm, recessed 6 cm
Fronts	2 door(s) · 1 drawer(s) · 0 niche(s)
Pulls	3 pcs (flower, black iron)

Fronts (W × H, cm)

Dw1	drawer · 63.4 × 38.4
D1	door · 63.4 × 64.9
D2	door · 63.4 × 64.9


Notes

• Opening for the built-in dishwasher: 60 × 86 cm (appliance 59 × 85 × 59), base at 50 cm from the floor; provide water, drain and power outlet.

Front view and side section · scale 1:25 (A4)

7 — Cabinet above fridge/freezer

Suite wall (left) · 336 to 540 cm from the front (glass) · installed at 205 cm from the floor

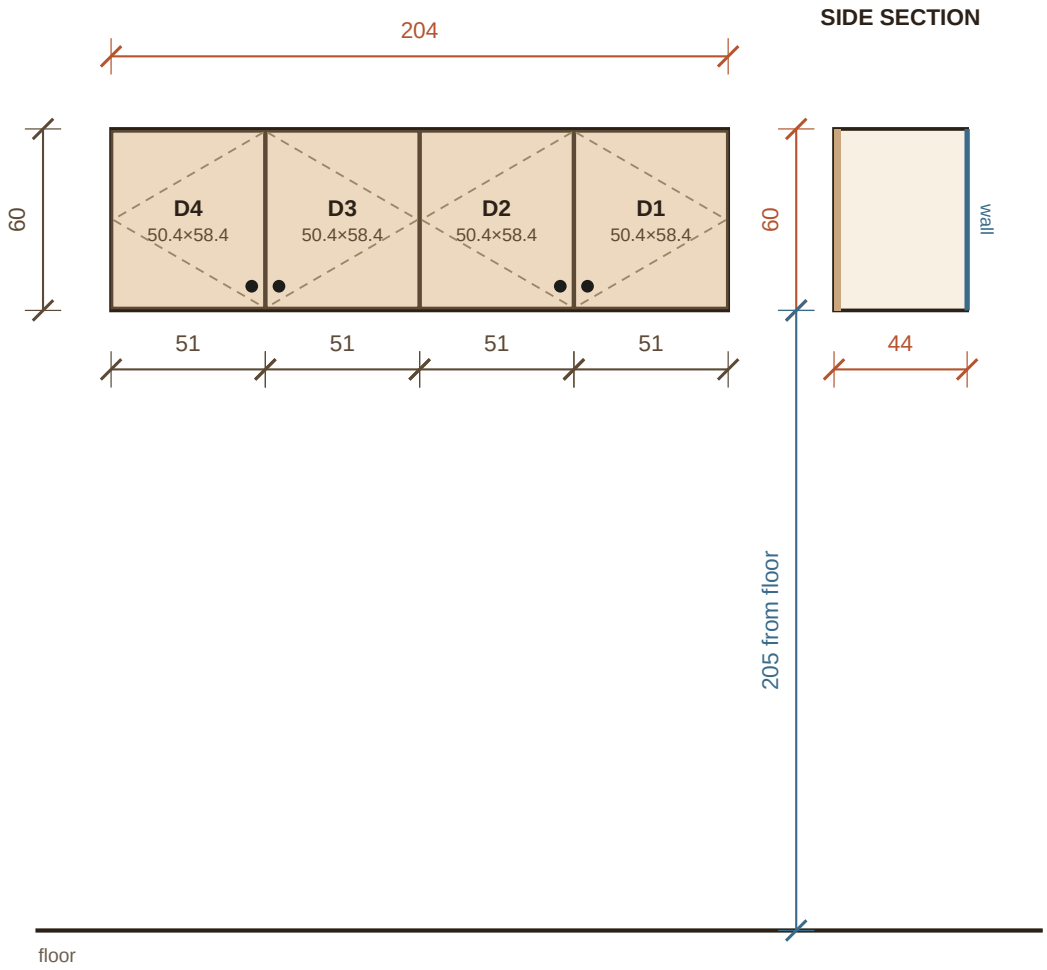

Specification


Overall size	204 (W) × 60 (H) × 44 (D) cm
Installation	wall-hung, bottom at 205 cm from the floor
Fixing	hidden rail/bracket on the wall
Fronts	4 door(s) · 0 drawer(s) · 0 niche(s)
Pulls	4 pcs (flower, black iron)

Fronts (W × H, cm)

D1	door · 50.4 × 58.4
D2	door · 50.4 × 58.4
D3	door · 50.4 × 58.4
D4	door · 50.4 × 58.4

8 — L-shaped cabinet – side

Right wall (large window) · 530 to 605 cm from the front (glass) · installed at 160 cm from the floor

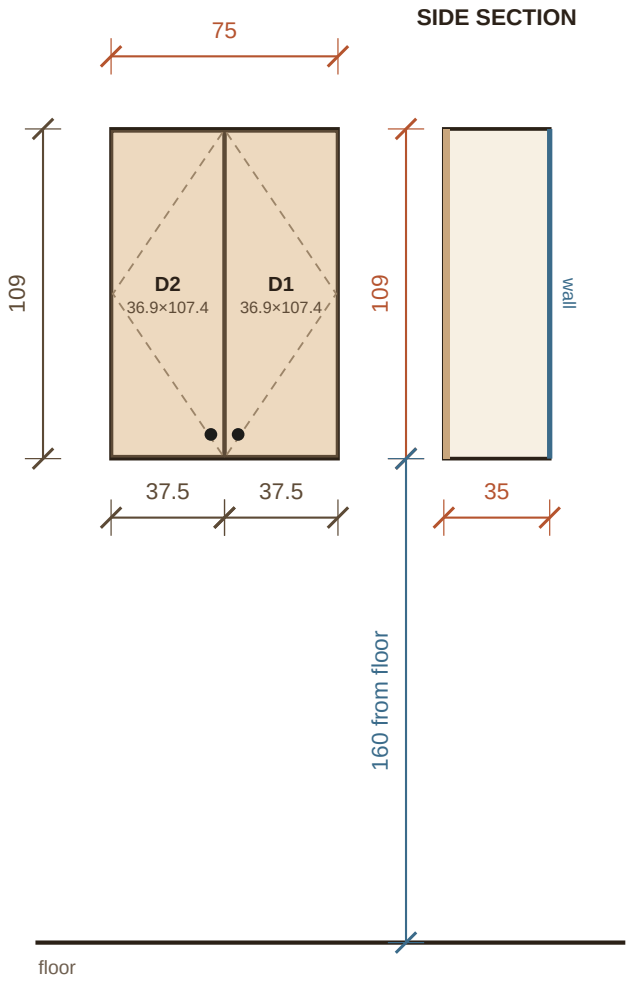

Specification


Overall size	75 (W) × 109 (H) × 35 (D) cm
Installation	wall-hung, bottom at 160 cm from the floor
Fixing	hidden rail/bracket on the wall
Fronts	2 door(s) · 0 drawer(s) · 0 niche(s)
Pulls	2 pcs (flower, black iron)

Fronts (W × H, cm)

D1	door · 36.9 × 107.4
D2	door · 36.9 × 107.4

9 — L-shaped cabinet – back (up to the window)

Back wall (sink) · 305.5 to 428 cm from the suite wall · installed at 160 cm from the floor

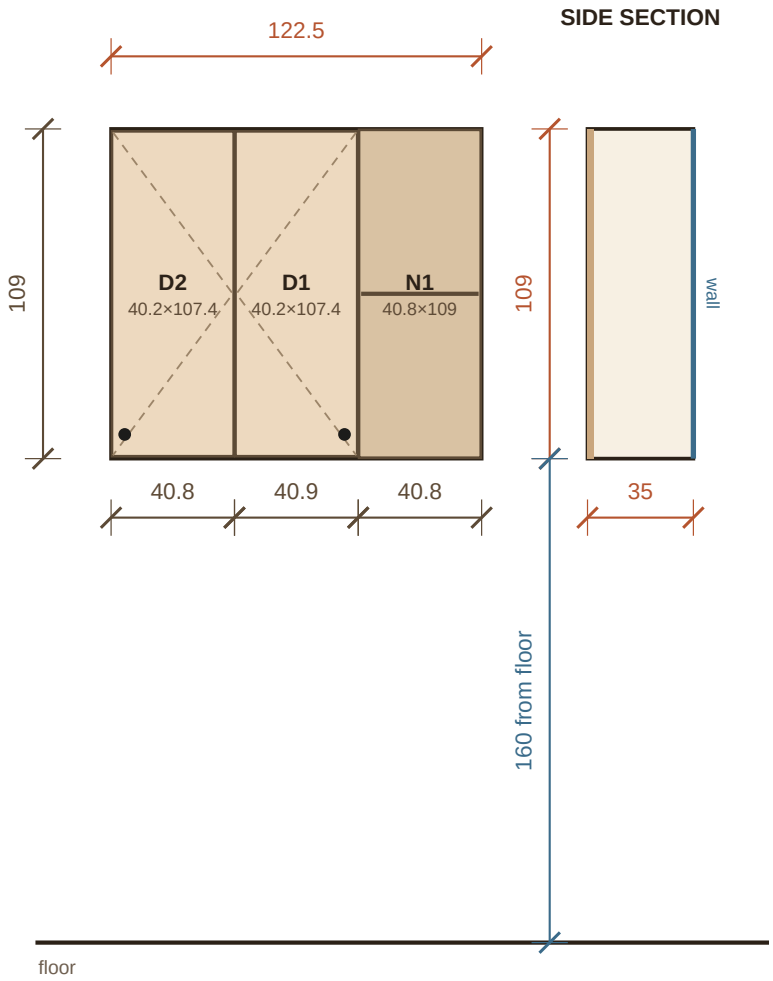

Specification

Overall size	122.5 (W) × 109 (H) × 35 (D) cm
Installation	wall-hung, bottom at 160 cm from the floor
Fixing	hidden rail/bracket on the wall
Fronts	2 door(s) · 0 drawer(s) · 1 niche(s)
Pulls	2 pcs (flower, black iron)

Fronts (W × H, cm)


N1	open bay · 40.2 × 108.4 · 1 shelf
D1	door · 40.2 × 107.4
D2	door · 40.2 × 107.4

Notes

• Open niche bay(s) with 1 shelf in the middle, dark wood back panel.

10 — Spice niches – side (up to the back wall)

Right wall (large window) · 530 to 640 cm from the front (glass) · installed at 124 cm from the floor

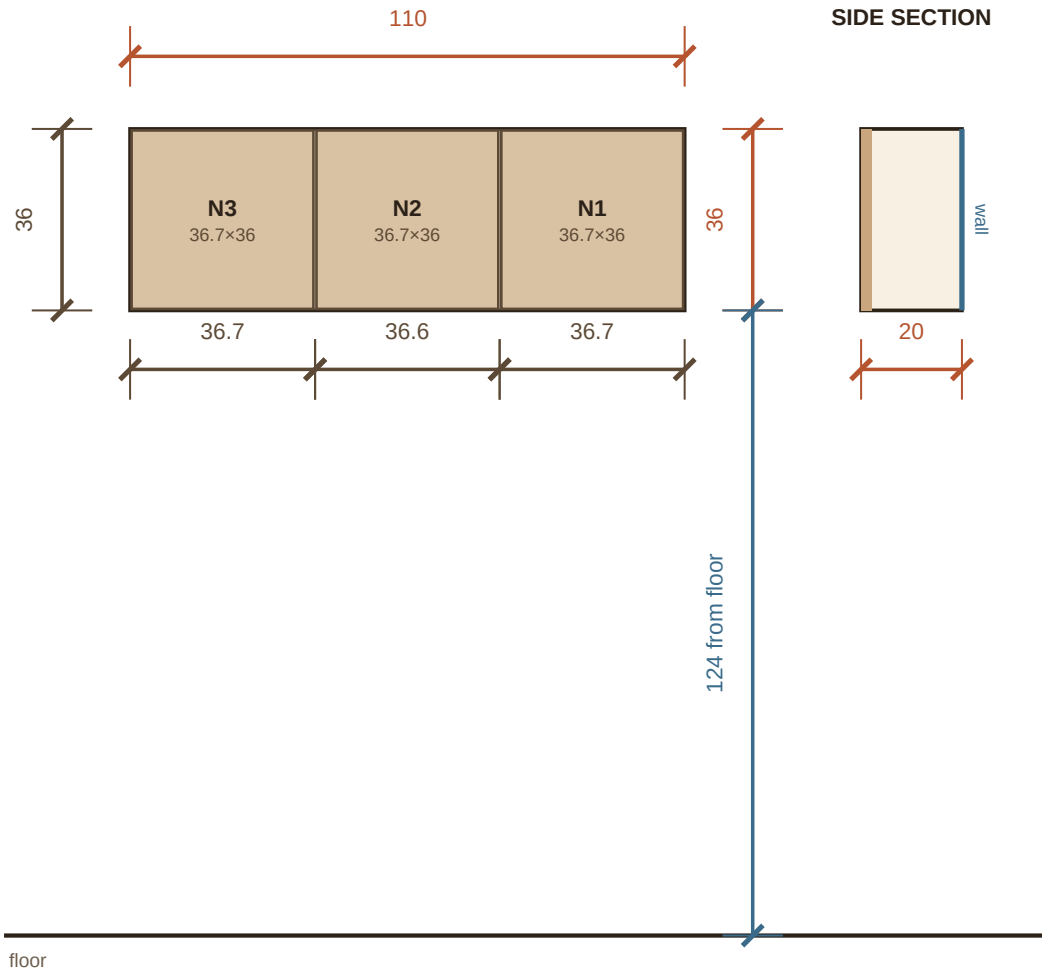

Specification

Overall size	110 (W) × 36 (H) × 20 (D) cm
Installation	wall-hung, bottom at 124 cm from the floor
Fixing	screwed to the wall (no doors)
Fronts	0 door(s) · 0 drawer(s) · 3 niche(s)
Pulls	0 pcs (flower, black iron)

Fronts (W × H, cm)

N1	open bay · 36.1 × 35.4
N2	open bay · 36.1 × 35.4
N3	open bay · 36.1 × 35.4

Notes

• Open spice niche: 3 bay(s), no intermediate shelf, 2 cm boards, 1.2 cm back panel.

Cut list — fronts (doors, drawers) and carcasses

Front sizes already net of the 3 mm gap on each side · check on site

Type	Width	Height	Qty.	Cabinets (No.)
drawer	73.5	41.5	1	4
drawer	70.5	41.5	1	1
drawer	117.5	40	1	5
drawer	63.5	38.5	1	6
drawer	73.5	16.5	2	4
drawer	70.5	16.5	2	1
drawer	117.5	16	2	5
door	40	107.5	2	9
door	37	107.5	2	8
door	57	75.5	2	3
door	48.5	75.5	1	2
door	35	75.5	2	1
door	63.5	65	2	6
door	50.5	58.5	4	7

Total: 15 doors · 10 drawers · 25 pulls · 4 niche bays

Carcasses (overall size)

No.	Cabinet	W × H × D
1	L-shaped counter (corner)	142 × 90 × 64
2	L-shaped counter (corner)	49 × 90 × 64
3	Sink counter (granilite)	115 × 90 × 62
4	L-shaped counter (corner)	140 × 90 × 62
5	Low cabinet next to the sideboard	120 × 86 × 56
6	Dishwasher tower (tall)	65 × 269 × 62
7	Cabinet above fridge/freezer	204 × 60 × 44
8	L-shaped cabinet – side	75 × 109 × 35
9	L-shaped cabinet – back (up to the window)	122.5 × 109 × 35
10	Spice niches – side (up to the back wall)	110 × 36 × 20

Reddish granilite countertops (stonemason)

Thickness 3 cm · 2 cm front overhang · 10 cm backsplash on the sides against the wall · dimensions in cm

No.	Counter	Top W × D × thick.	Cutouts / recess	Backsplash
1	L-shaped counter (corner)	142 × 66 × 3	—	no backsplash
2	L-shaped counter (corner)	49 × 66 × 3	—	back 49 cm
3	Sink counter (granilite)	115 × 64 × 3	sink: cutout 66 × 36 at 14 from the left edge (top view); 1.5 cm recess around it (left 4, right 78, front 3.5, back 7.5)	back 115 cm
4	L-shaped counter (corner)	140 × 64 × 3	—	back 140 cm + side 62 cm